# TEATRO Firjan SESI CENTRO

Atualizado em 30/10/2024
(por Camila)

## Descrição

| | | | | | |
|---|---|---|---|---|---|
| Palco | Italiano | Boca de cena | Largura | 9,70m |  |
| | | | Altura | 4,48m | |
| | | Procênio | | 2,32m | |
| | | Profundidade | | 7,30m | |
| | | Pé direito | | 5,49m | |
| | | Urdimento | | 0,30m | |
| | | Coxia | Esquerda | 4m x 5,50m | |
| | | | Direira | 0,80m x 11m | |
| Lugares | | Plateia | 246 | | considerando que 7 lugares são destinados a cadeirantes, 3 a obesos e 4 a deficientes visuais |
| | | Balcão | 92 | | |
| | | Total | 338 | | |

## Iluminação

### Refletores

| | Quantidade | |
|---|---|---|
| **Elipsoidal ETC 750 Zoom 50°** | 2 | Com Iris, porta gobo e porta gelatina |
| **Elipsoidal 650 CCT** | 1 | Sem íris e porta Gobo abertura de 21° a 36° |
| **Fresnel 1000 Telem** | 4 | |
| **Fresnel 650 CCT** | 2 | |
| **PC 1000 Telem** | 8 | |
| **PC 650 CCT** | 2 | |
| **Source Four** | 10 | Com respectivo jogo de lente#1, 2, 5,6 |
| **PAR** | 6 | |
| **Ribalta de Led** | 5 | 3 RGB e 2 RGBW |
| **Total de Peças** | 40 | |

### Materiais Fixos

| | | | | |
|---|---|---|---|---|
| Mesa de Comando | 1 | ETC ION | 1024 Canais | |
| | 1 | ETC Express | 24/48 Canais | |
| Dimmer de Potência | 11 | Ceitronic | 124 Linhas | 4Kw por canal |
| Geral Branca | 6 | Sourse four | Dividida em esquerda, Meio e direita | |
| PAR | 10 | Generic de 1W 3MM | Fixo na vara Junto com os movings | |
| Moving Beam | 5 | Moving Beam 16R | 3 moving fixos nas Varas de Palco e 1 Moving Central na varanda de Geral | |
| Canhão seguidor | 1 | Holler | DMX1200 | |

### Caracteristias fisicas do palco

| | | |
|---|---|---|
| Varas de Iluminação | 4 | Com 12 tomadas steck em cada |
| | 2 | Nas Laterais do Palco com 6 steck em cada |

Cabine 2563-4006 Paulo Vieira 98678-7095 Osvaldo Ribeiro 98883-7546

# TEATRO Firjan SESI CENTRO

Atualizado em 30/10/2024
(por Camila)

| | | | | | | |
|---|---|---|---|---|---|---|
| Ponte de Iluminação | | 1 | Com 24 tomadas steck em cada | | | |
| Barras de Luz | | 2 | Fixa nas laterais da plateia com 6 tomadas steck em cada | | | |
| | | 2 | Nos reguladores Horizontais Com 6 Tomadas steck Cada | | | |
| ***Multimidia*** | | | | | | |
| Projetor de Vídeo | 1 | Fixo | Proscênio | Benq SP920P | Luminosidade 6.000 Ansi Lumens, Resolução, 1024x768 (XGA), Formato de Tela4:3, Contraste 4.000:1 ,Tecnologia DLP, Conecxão VGA | |
| | 1 | Movel | Balcão | Benq SP920P | Luminosidade 6.000 Ansi Lumens, Resolução, 1024x768 (XGA), Formato de Tela4:3, Contraste 4.000:1 ,Tecnologia DLP, Conecxão VGA e HDMI | |
| | 1 | Fixo | Varanda | | | |
| Tela de Projeção | 1 | Fixo | Proscênio | | Retrátil de 150" Automatico | |
| | 1 | Fixo | palco | | Retrátil de 150" | |
| ***Audio*** | | | | | | |
| Console de mixagem | | 2 | Yamaha | | digital CL 5 | 72 Canais |
| | | 1 | | | digital M7CL | 32 Canais |
| | | 1 | | | digital 01V | 16 Canais |
| CDJ | | 2 | Pioneer | | 400 Limited | USB MP3 |
| STAGE BOX | | 2 | Yamaha | | RIO 3224-D | 32 in x 16 out |
| CAIXAS DE PA | | 10 | MINA | | LINE ARRAY MEYER SOUND | |
| Caixas Subwoofer | | 4 | MEYER SOUND | | HP-500 | |
| Processador de sistema | | 1 | GALILEO | | | |
| Rack de amplificação | | 2 | Cíclotron Techvox | | classe-AB para Side-Fill | 6 Vias Independentes |
| Caixas acústicas | | 4 | BOSE 502 | | Side-Fill | |
| | | 4 | FZ-102P | | Retorno | |
| | | 2 | Fz-108 | | | |
| | | 6 | MEYER SOUND MJF-212 A | | | |
| | | 2 | Sub-Woofer 502 B | | Side-Fill | |
| | | 2 | Attak Ativas | | | |
| | | 2 | Yamaha-HSM50 | | Referencia na cabine | |
| Amplificador | | 2 | Behringer | | Power Play-8000 | Headphone |
| Microfone | | 4 | AKG | | C414 | |
| | | 2 | | | Condensadores 451 | |
| | | 4 | | | D112 | |
| | | 8 | Shure UHF | | Sem fio Microfone Beta58 UHF-R | |
| | | 4 | Sennheiser | | Sem fio EW 100 G3 | |
| | | 12 | SHURE | | Dinâmicos SM 58 | |
| | | 8 | | | Dinâmicos SM 57 | |
| | | 2 | | | Dinâmicos PG 52 | |
| | | 2 | | | Condensadores SM 81 | |
| | | 6 | | | Beta 98 | |
| | | 3 | Áudio-técnica | | ATW-1101/HTZ-HT | Head-set |
| | | 2 | Sennheiser | | Dinâmicos MD 421 | |
| In-Near | | 4 | Shure | | PSM 1000 | |
| Fones | | 5 | AKG | | 414 p | |
| | | 1 | Porta Pro | | | |
| | | 5 | | | Ultra-DI 100 | Ativa |

Cabine 2563-4006 Paulo Vieira 98678-7095 Osvaldo Ribeiro 98883-7546

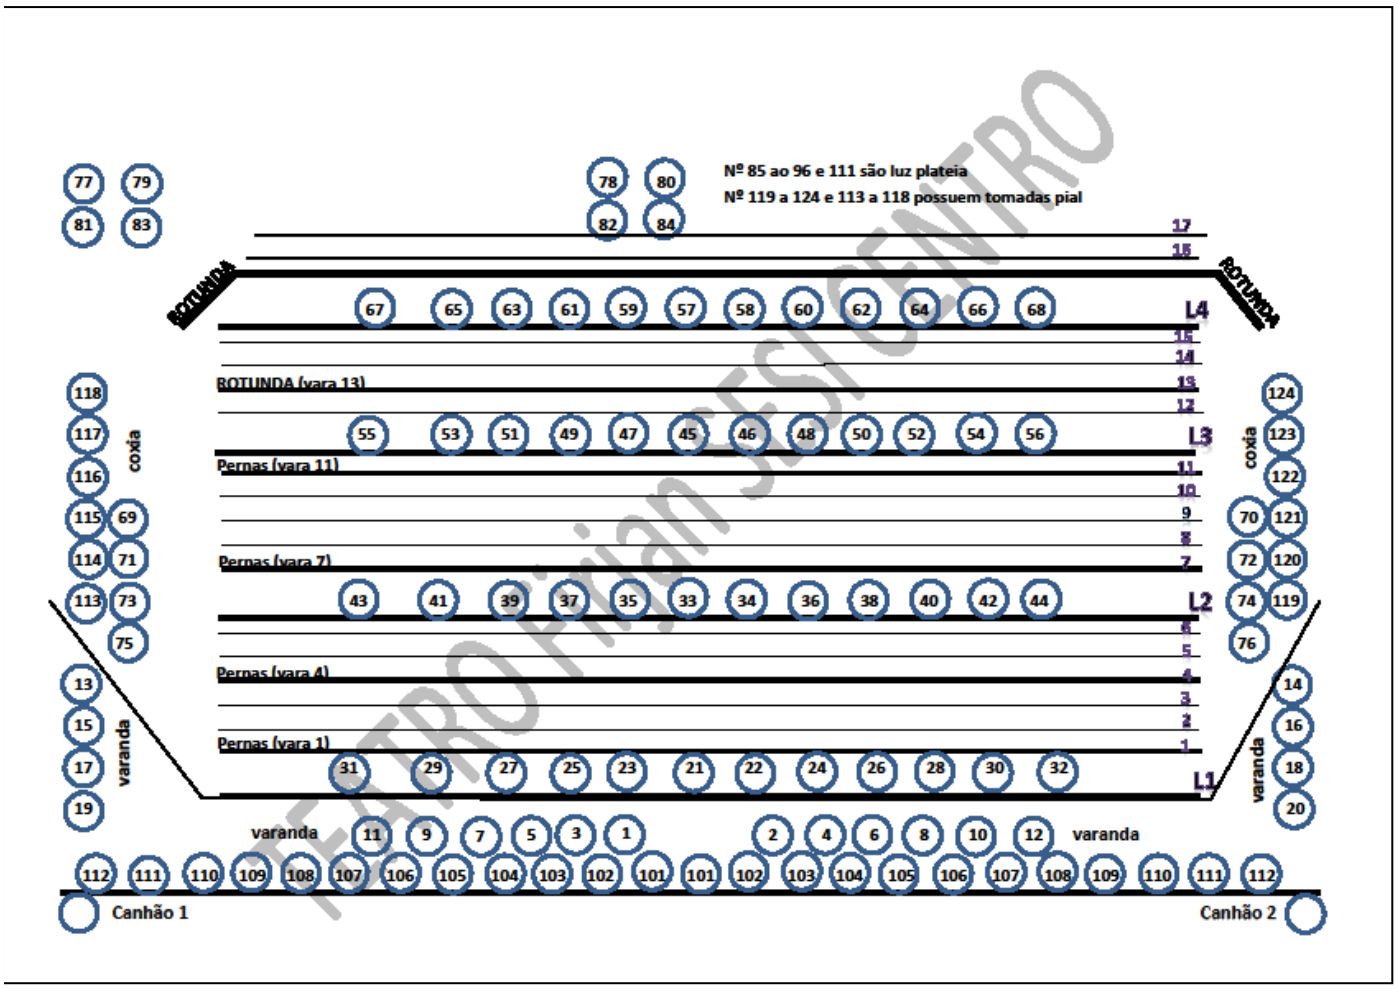
# TEATRO Firjan SESI CENTRO

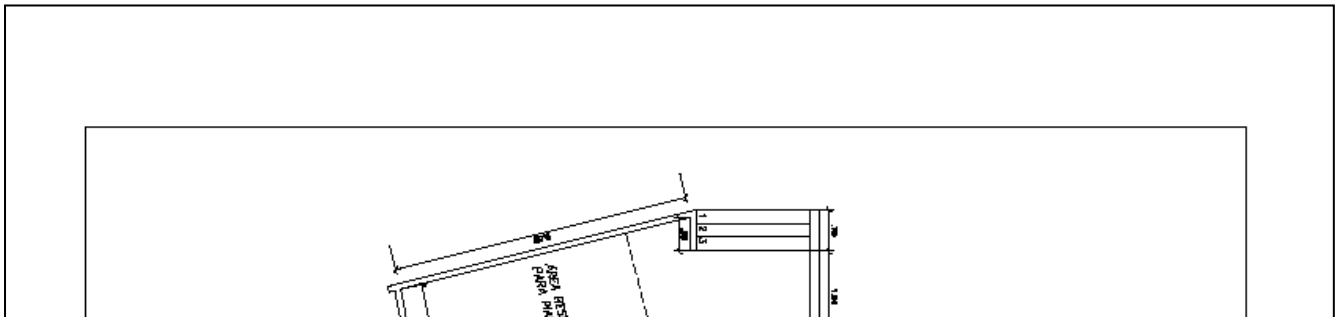
Atualizado em 30/10/2024
(por Camila)

| | | | | |
|---|---|---|---|---|
| Direct-box | 2 | Behringer | Ultra-DI 600P | Passiva |
| | 2 | | Ultra-DI Pro 800 | Ativa |
| Pedestais | 4 | | Mesa | |
| | 6 | RMV | Pequeno | |
| | 14 | | Girafa | |
| Garra de Microfone | 3 | | | |
| Estante de Partitura | 6 | RMV | Madeira | |
| | 2 | | Metal | |
| ***Backline*** | | | | |
| Amplificador | 1 | Roland | Jazz Chorus-120 | Guitarra |
| | 1 | Fender Twin | | |
| | | | | |
| | | | | Bateria completa GRETSCH CATALINA BIRCH |
| Caixa | 1 | | 14" x 5,5" | |
| Tom | 1 | | 10" x 7" | |
| | 1 | | 12" x 8" | |
| Bumbo | 1 | | 22" x 16" | |
| Surdo | 1 | | 16" x 14" | |
| Estante | 2 | Gretsch | | |

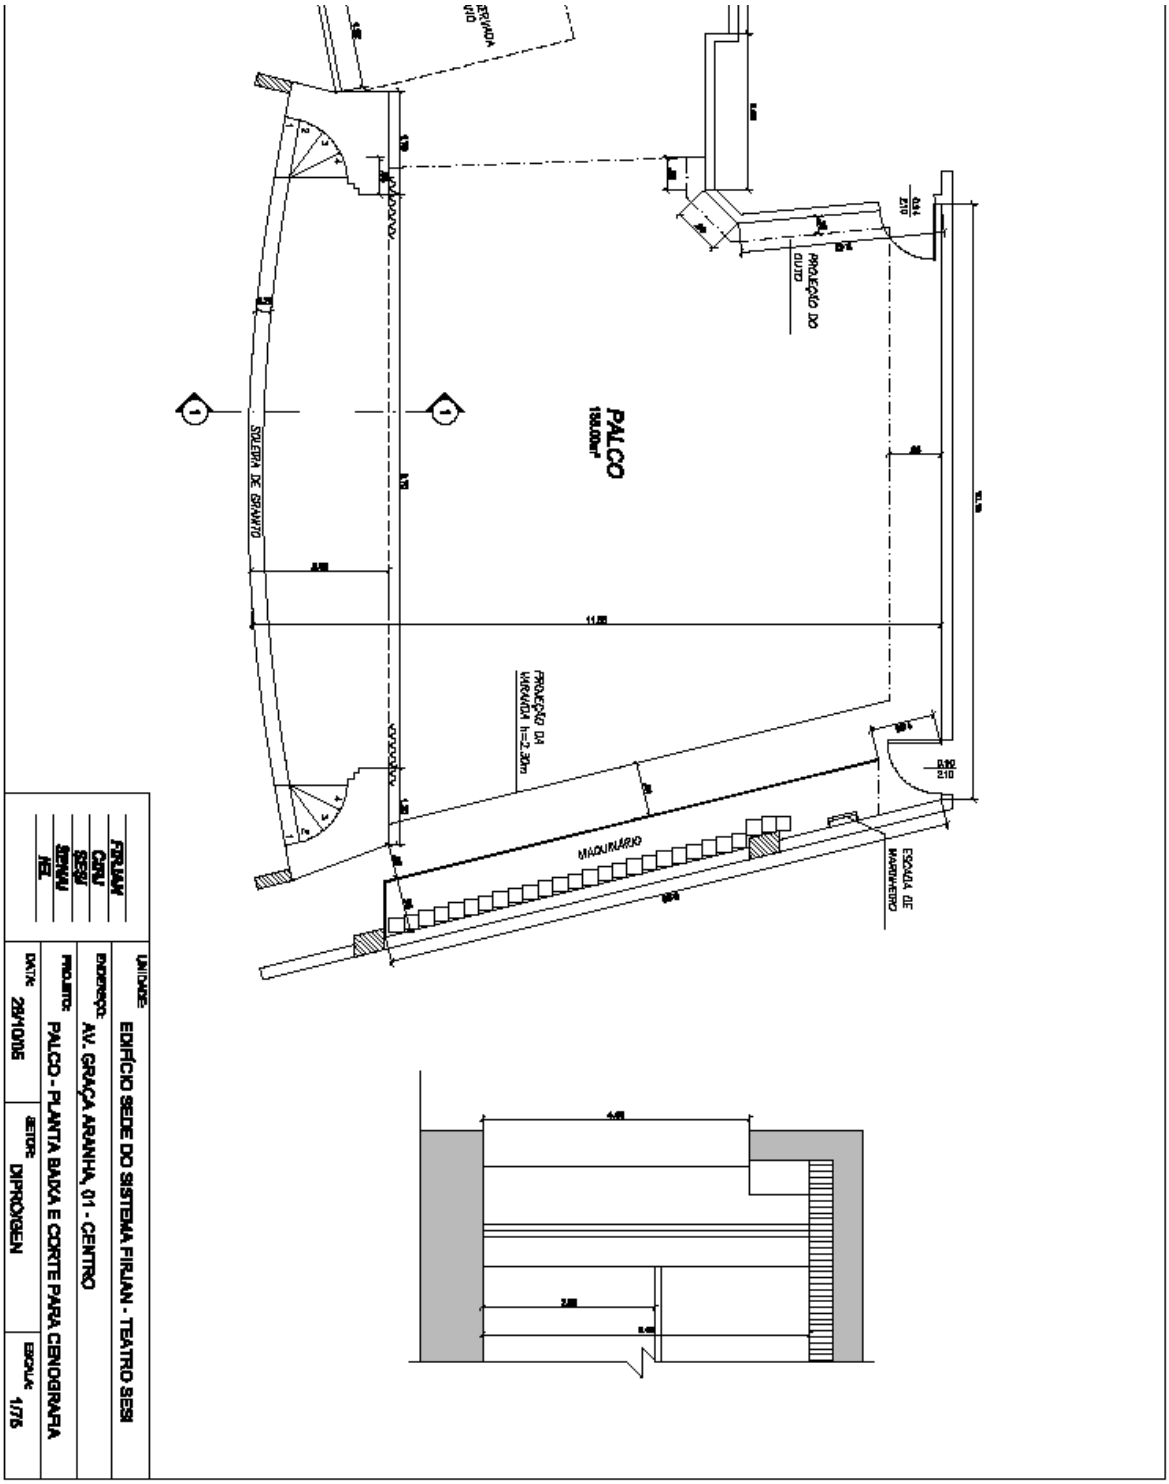
# TEATRO Firjan SESI CENTRO

Atualizado em 30/10/2024
(por Camila)



Cabine 2563-4006 Paulo Vieira 98678-7095 Osvaldo Ribeiro 98883-7546


PALCO
188,00m²
SOLEIRA DE GRANITO
PROJEÇÃO DA VERANDA h=2,30m
MADEIRAMENTO
ESCADA DE MARINHEIRO
PROJEÇÃO DO QUITO
VERANDA
FIRJAN
CIRJ
SESI
SENAI
IEL
UNIDADE: EDIFÍCIO SEDE DO SISTEMA FIRJAN - TEATRO SESI
ENDEREÇO: AV. GRAÇA ARANHA, 01 - CENTRO
PROJETO: PALCO - PLANTA BAIXA E CORTE PARA CENOGRAFIA
DATA: 28/10/2015
SETOR: DIPROXGEN
ESCALA: 1/75